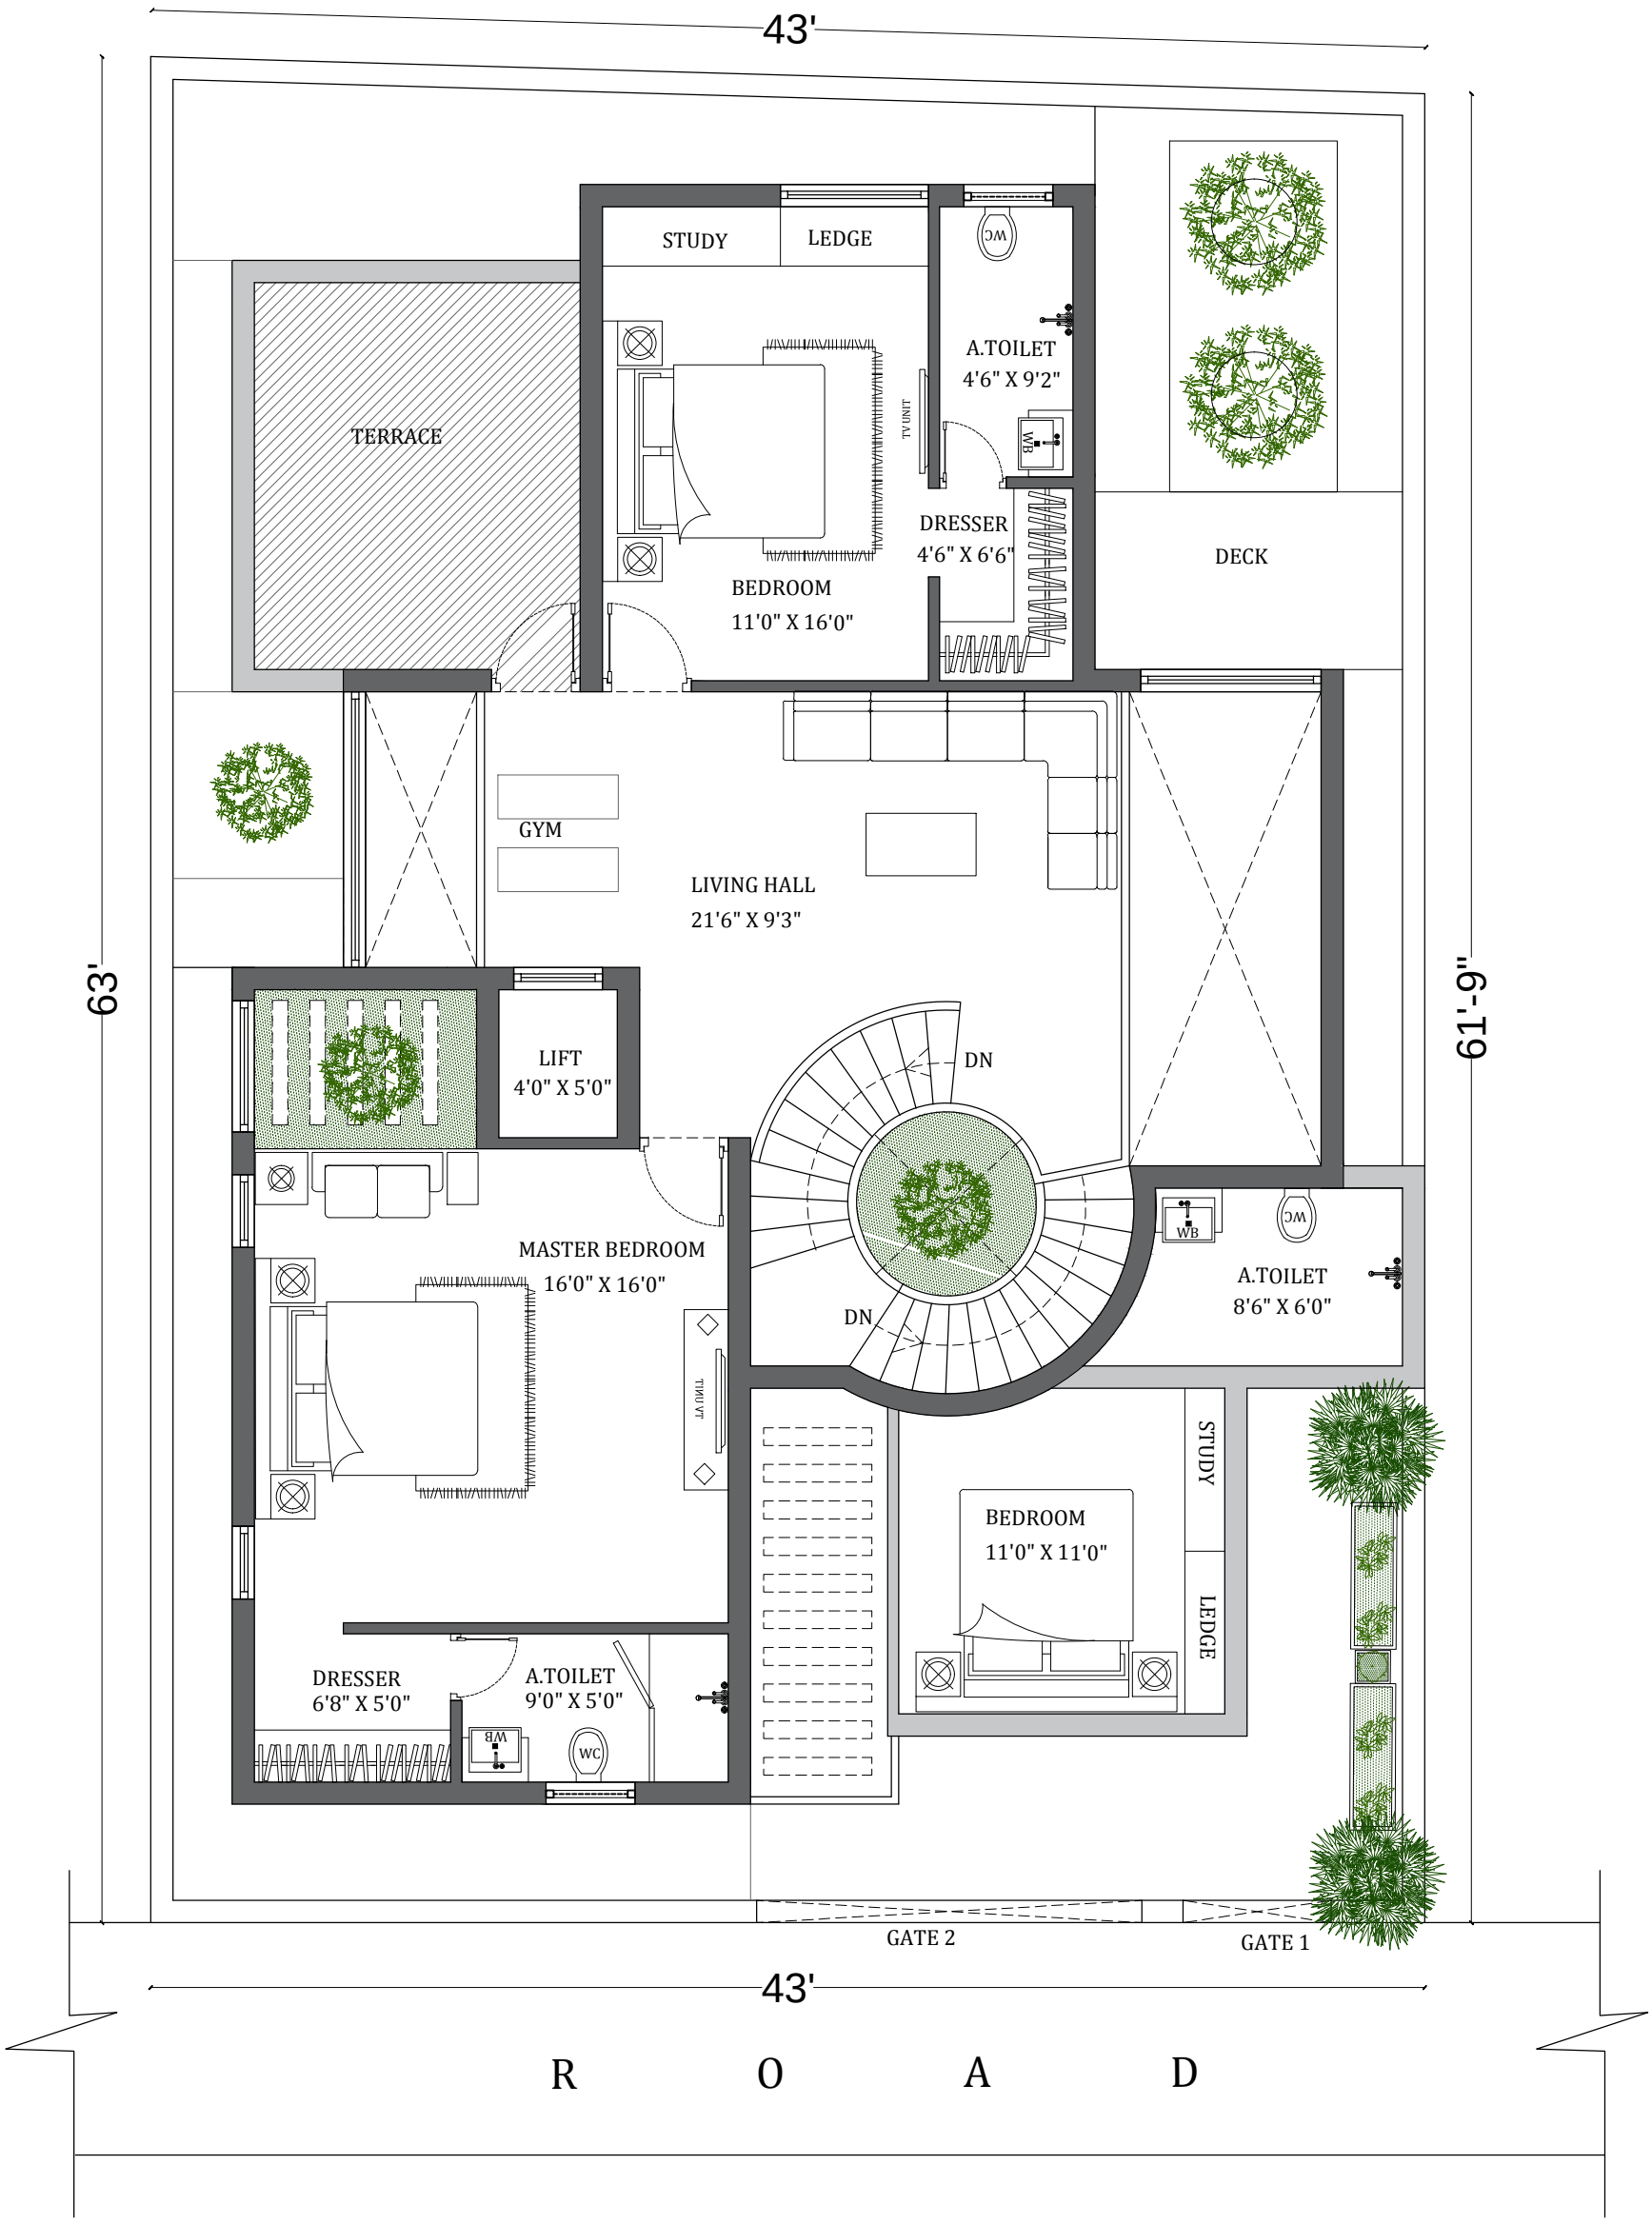

FIRST FLOOR PLAN

N

DRAWING NO	AR-SC.D-321
DRAWING DATE	07-08-2021
DRAWN BY	AR.SURUTHI
CHECKED BY	
REVISED BY	
REVISION DATE	13-08-2021
DRAWING TITLE	ARCHITECTURAL FLOOR PLAN

PRINTING INSTRUCTIONS

A0	A1	A2	A3	A4
			■	

DWG REVISION NO : **0**

LOCATION : SANGLIYANDAPURAM , TRICHY

PROJECT NAME

MR.ASHIK RESIDENCE

AREA STATEMENT

SITE AREA	: 2682.3 SQ.FT
GF AREA	: 1668.9SQ.FT
PORCH	: 382.9 SQ.FT
MEZZ AREA	: 428.3 SQ.FT
FF AREA	: 1357.3 SQ.FT

CONTACT Ar.Syed khalilullah
97G/6B/2nd street
Teachers colony,Tuticorin-03
9629507035, ph :-0461-2337035
info.inaassociates@gmail.com

1) ALL THE DIMENSIONS ARE GIVEN IN FEET AND INCHES.
2) DO NOT SCALE THE DRAWINGS.
3) THIS DRAWING IS MEANT TO BE READ, NOT MEASURED.
4) ALL THE DIMENSIONS MUST BE CHECKED AT SITE AND DISCREPANCIES VERIFIED WITH THE ARCHITECT.
5) THIS DRAWING IS THE PROPERTY OF THE ARCHITECT. IT SHALL NOT BE COPIED, REPRODUCED OR USED FOR ANY OTHER PURPOSE THAN SPECIFIED.

INA Associates